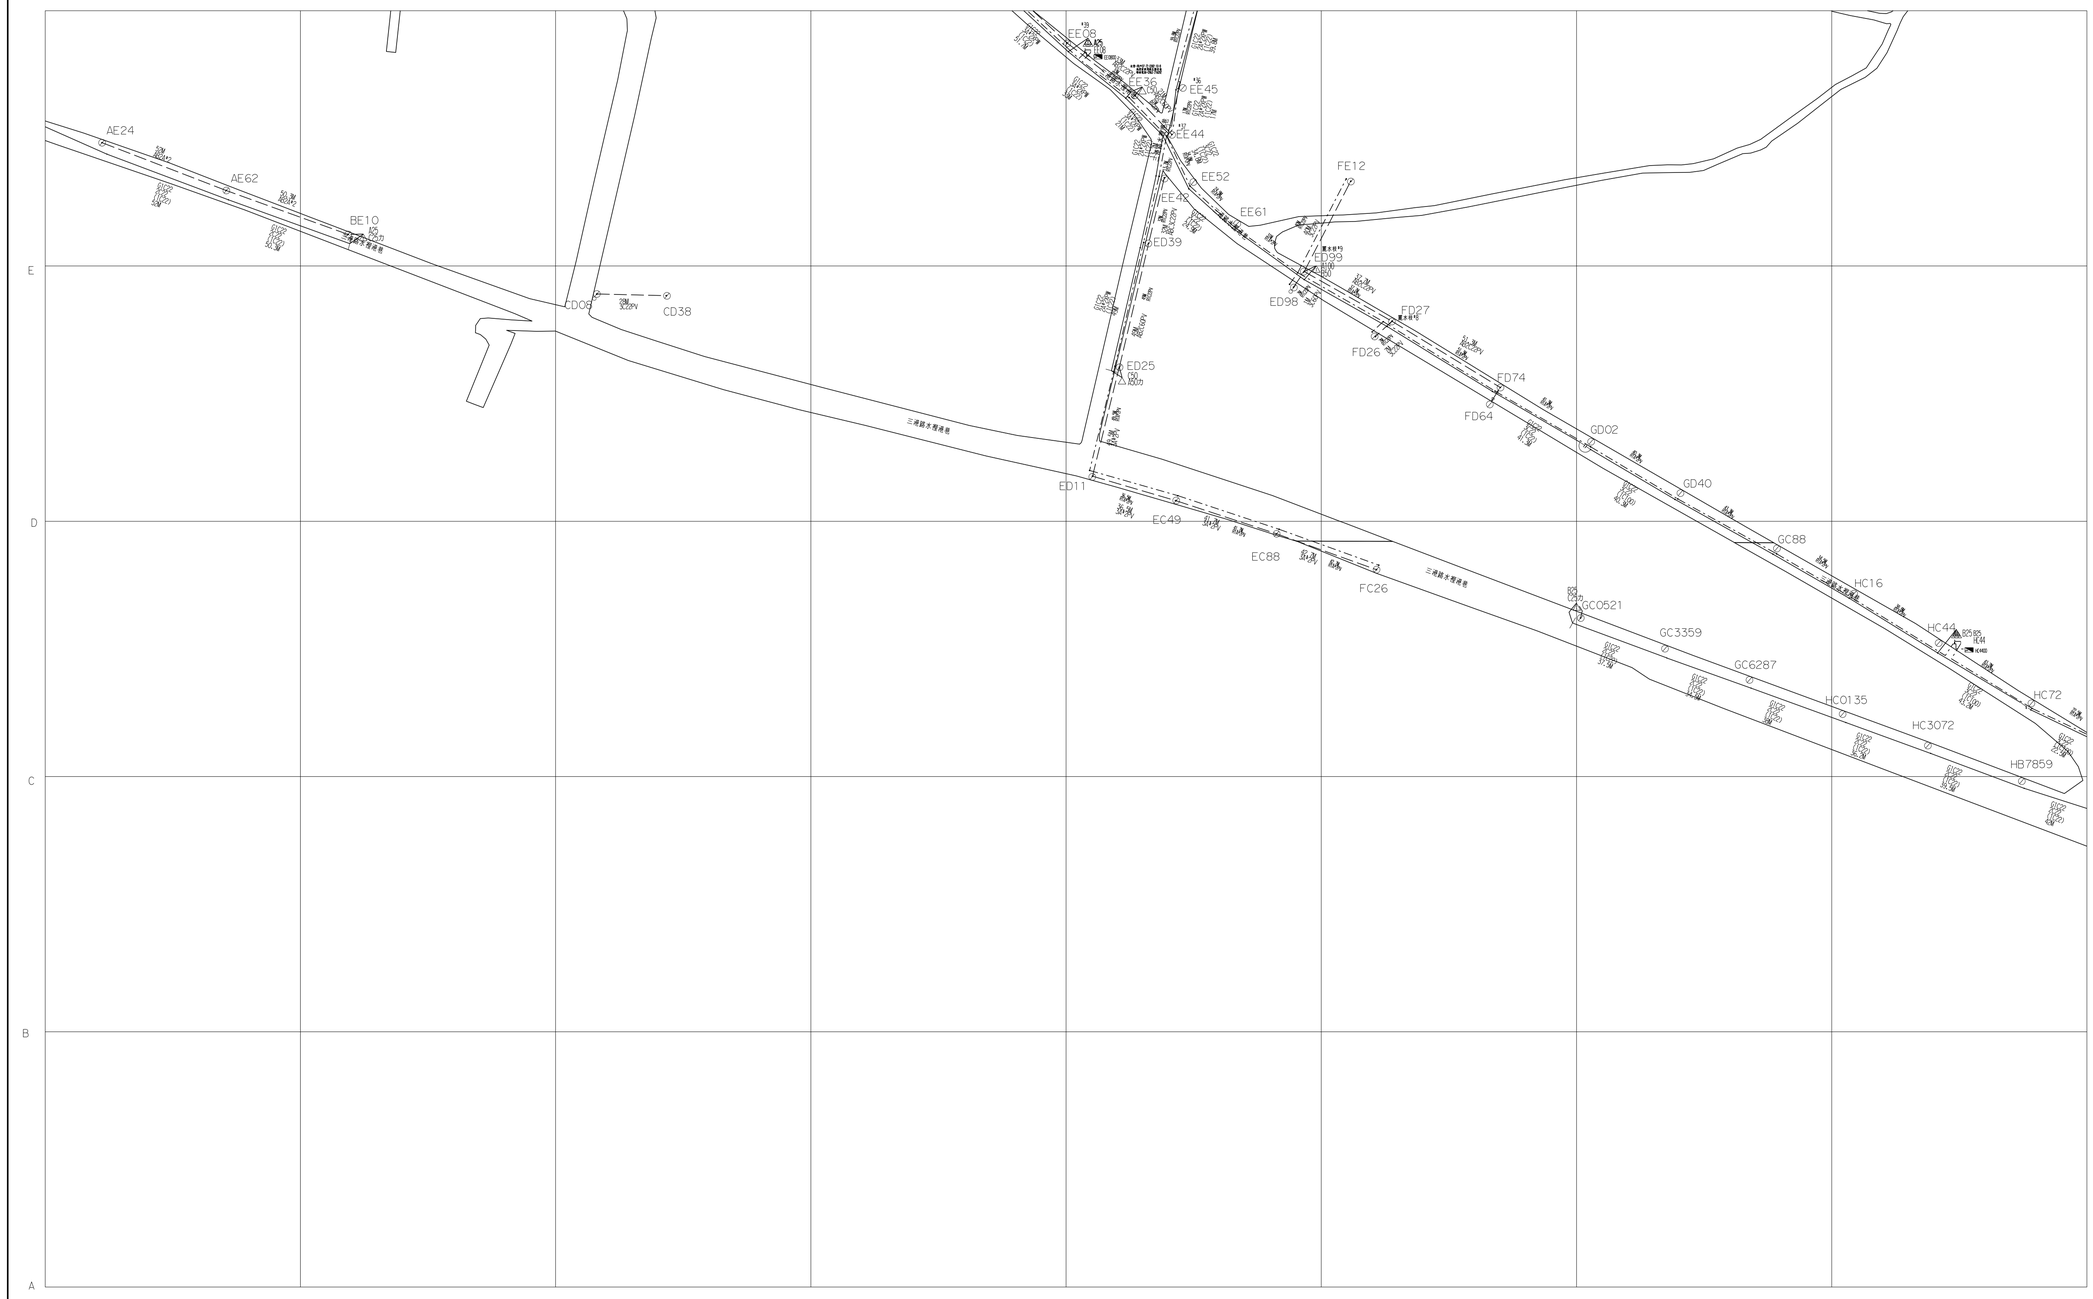


修正者	修正日期

供電變電所	
變電所別	供電饋線別

3455	3555	3655
3454	3554	3654
3453	3553	3653

比例 1:1200

0 50 100M

臺灣電力公司臺中區營業處

校對		批准	
製圖		製圖年月	
圖號	G3554 HT-LT/OH		