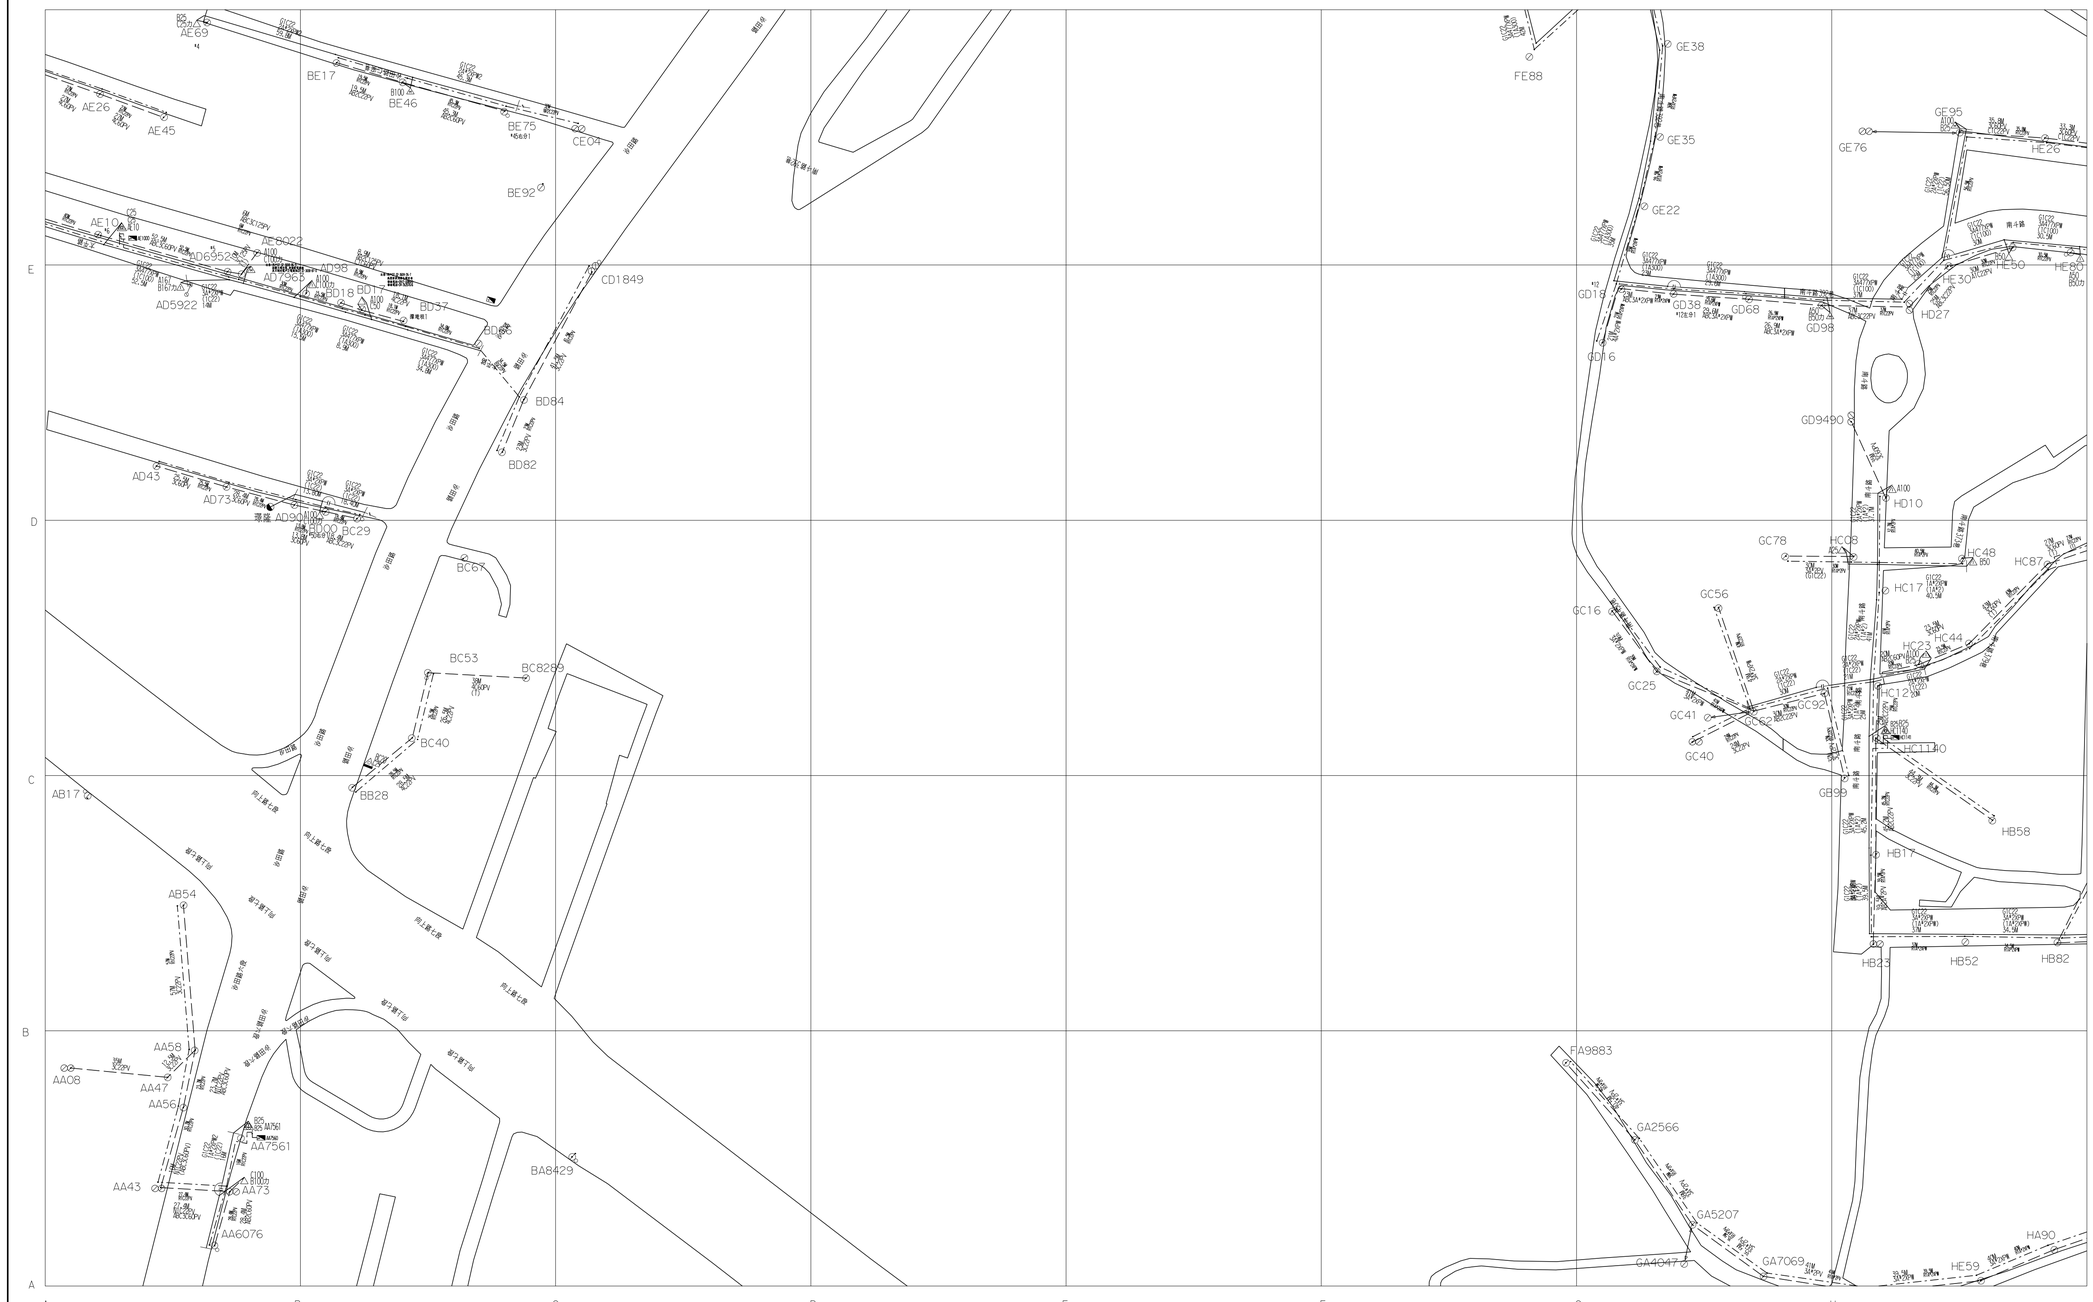


修正者	修正日期

供電變電所	
變電所別	供電饋線別

4159	4259	4359
4158	4258	4358
4157	4257	4357

比例 1:1200

0 50 100M

臺灣電力公司臺中區營業處

校對		批准	
製圖		製圖年月	
圖號	G4258 HT-LT/OH		