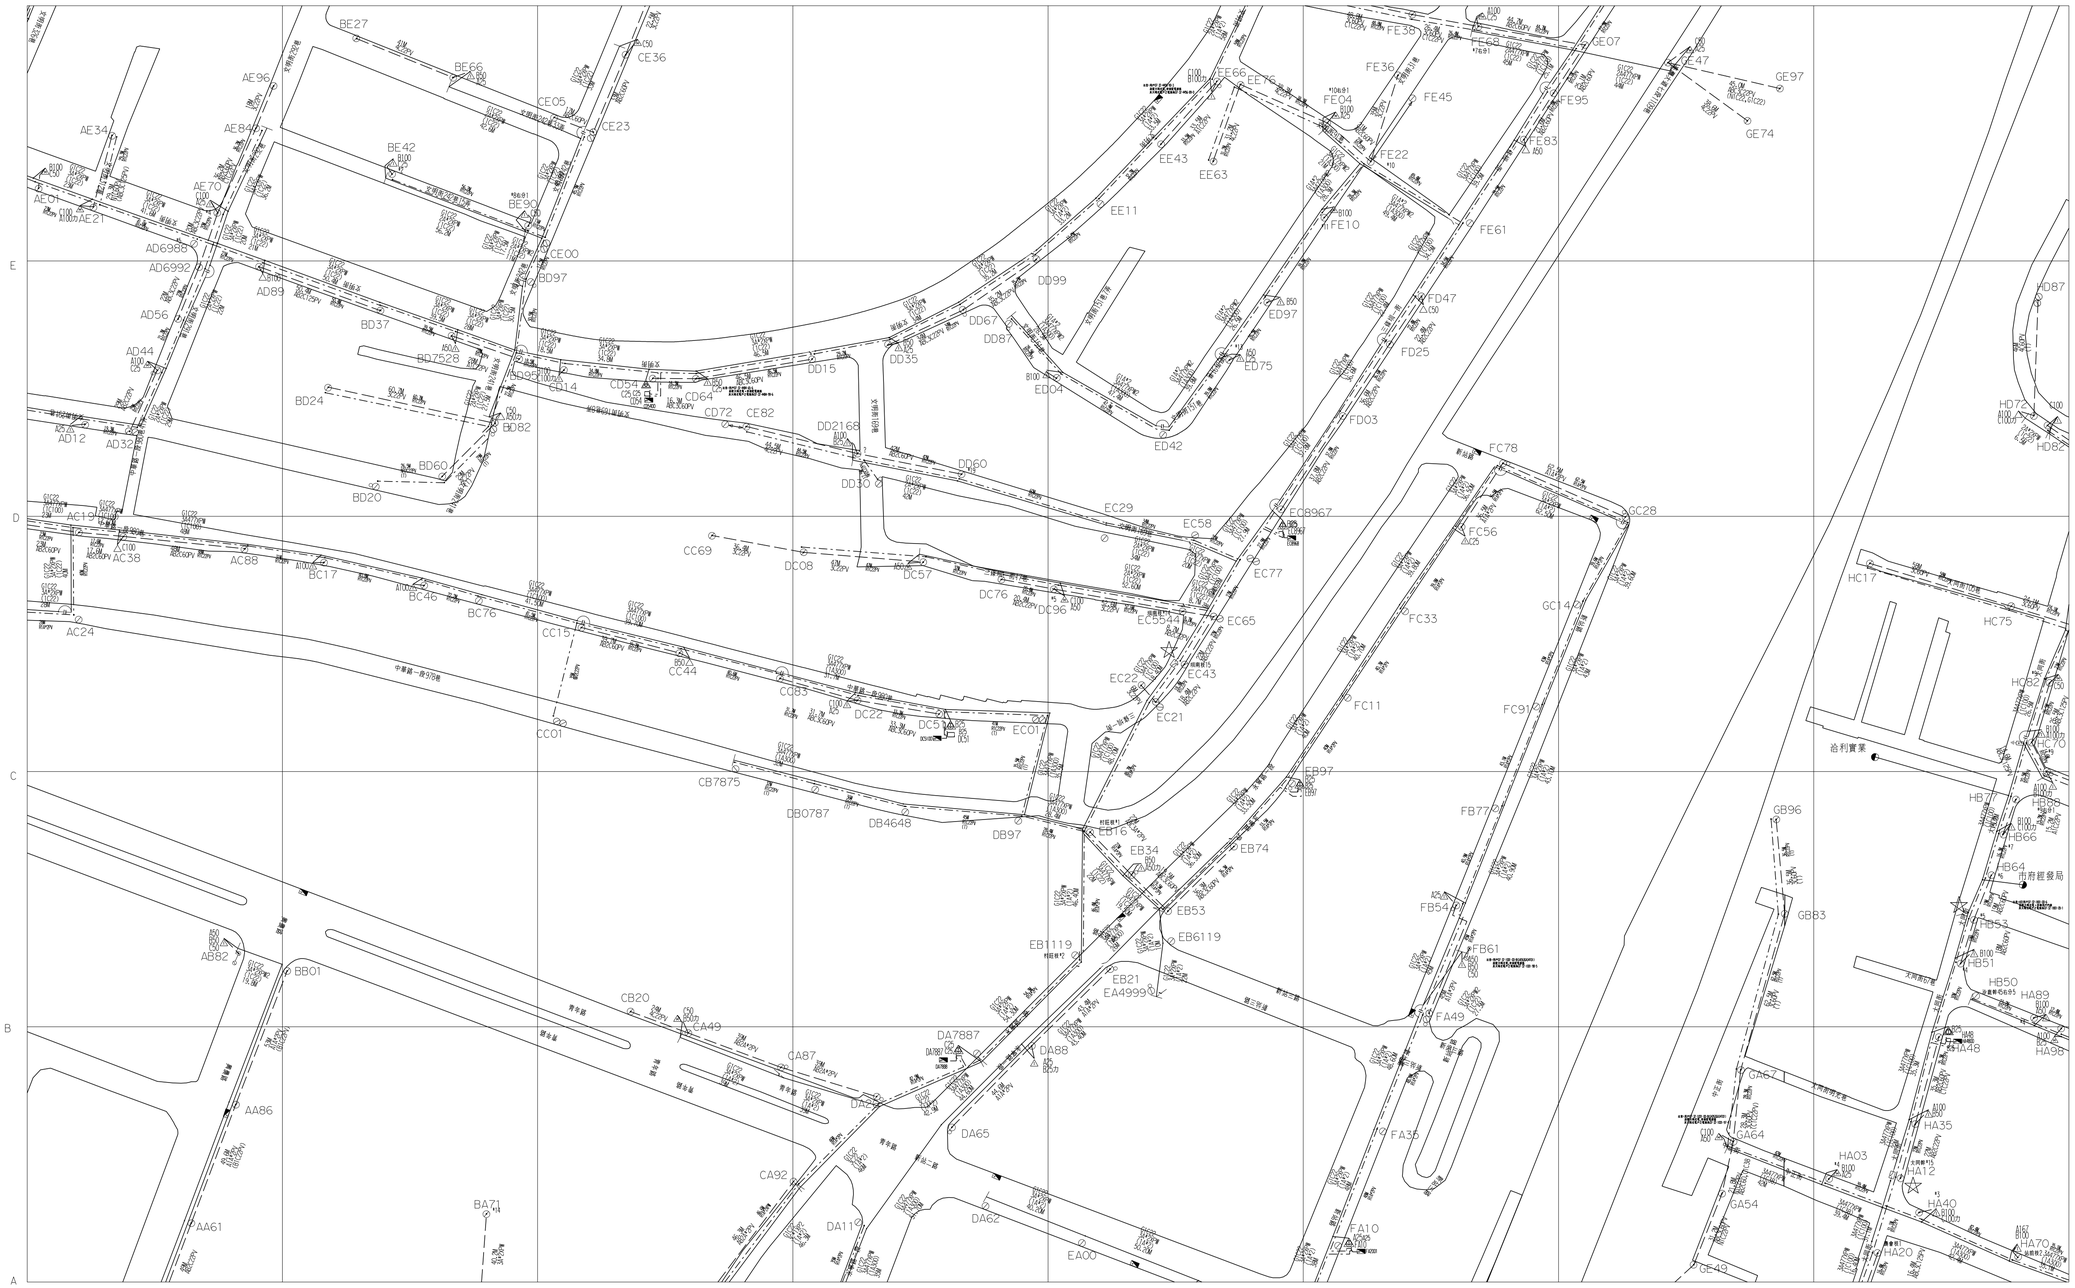


修正者	修正日期

供電變電所	
變電所別	供電饋線別

4164	4264	4364
4163	4263	4363
4162	4262	4362

比例 1:1200

0 50 100M

臺灣電力公司臺中區營業處

校對		批准	
製圖		製圖年月	
圖號	G4263 HT-LT/OH		