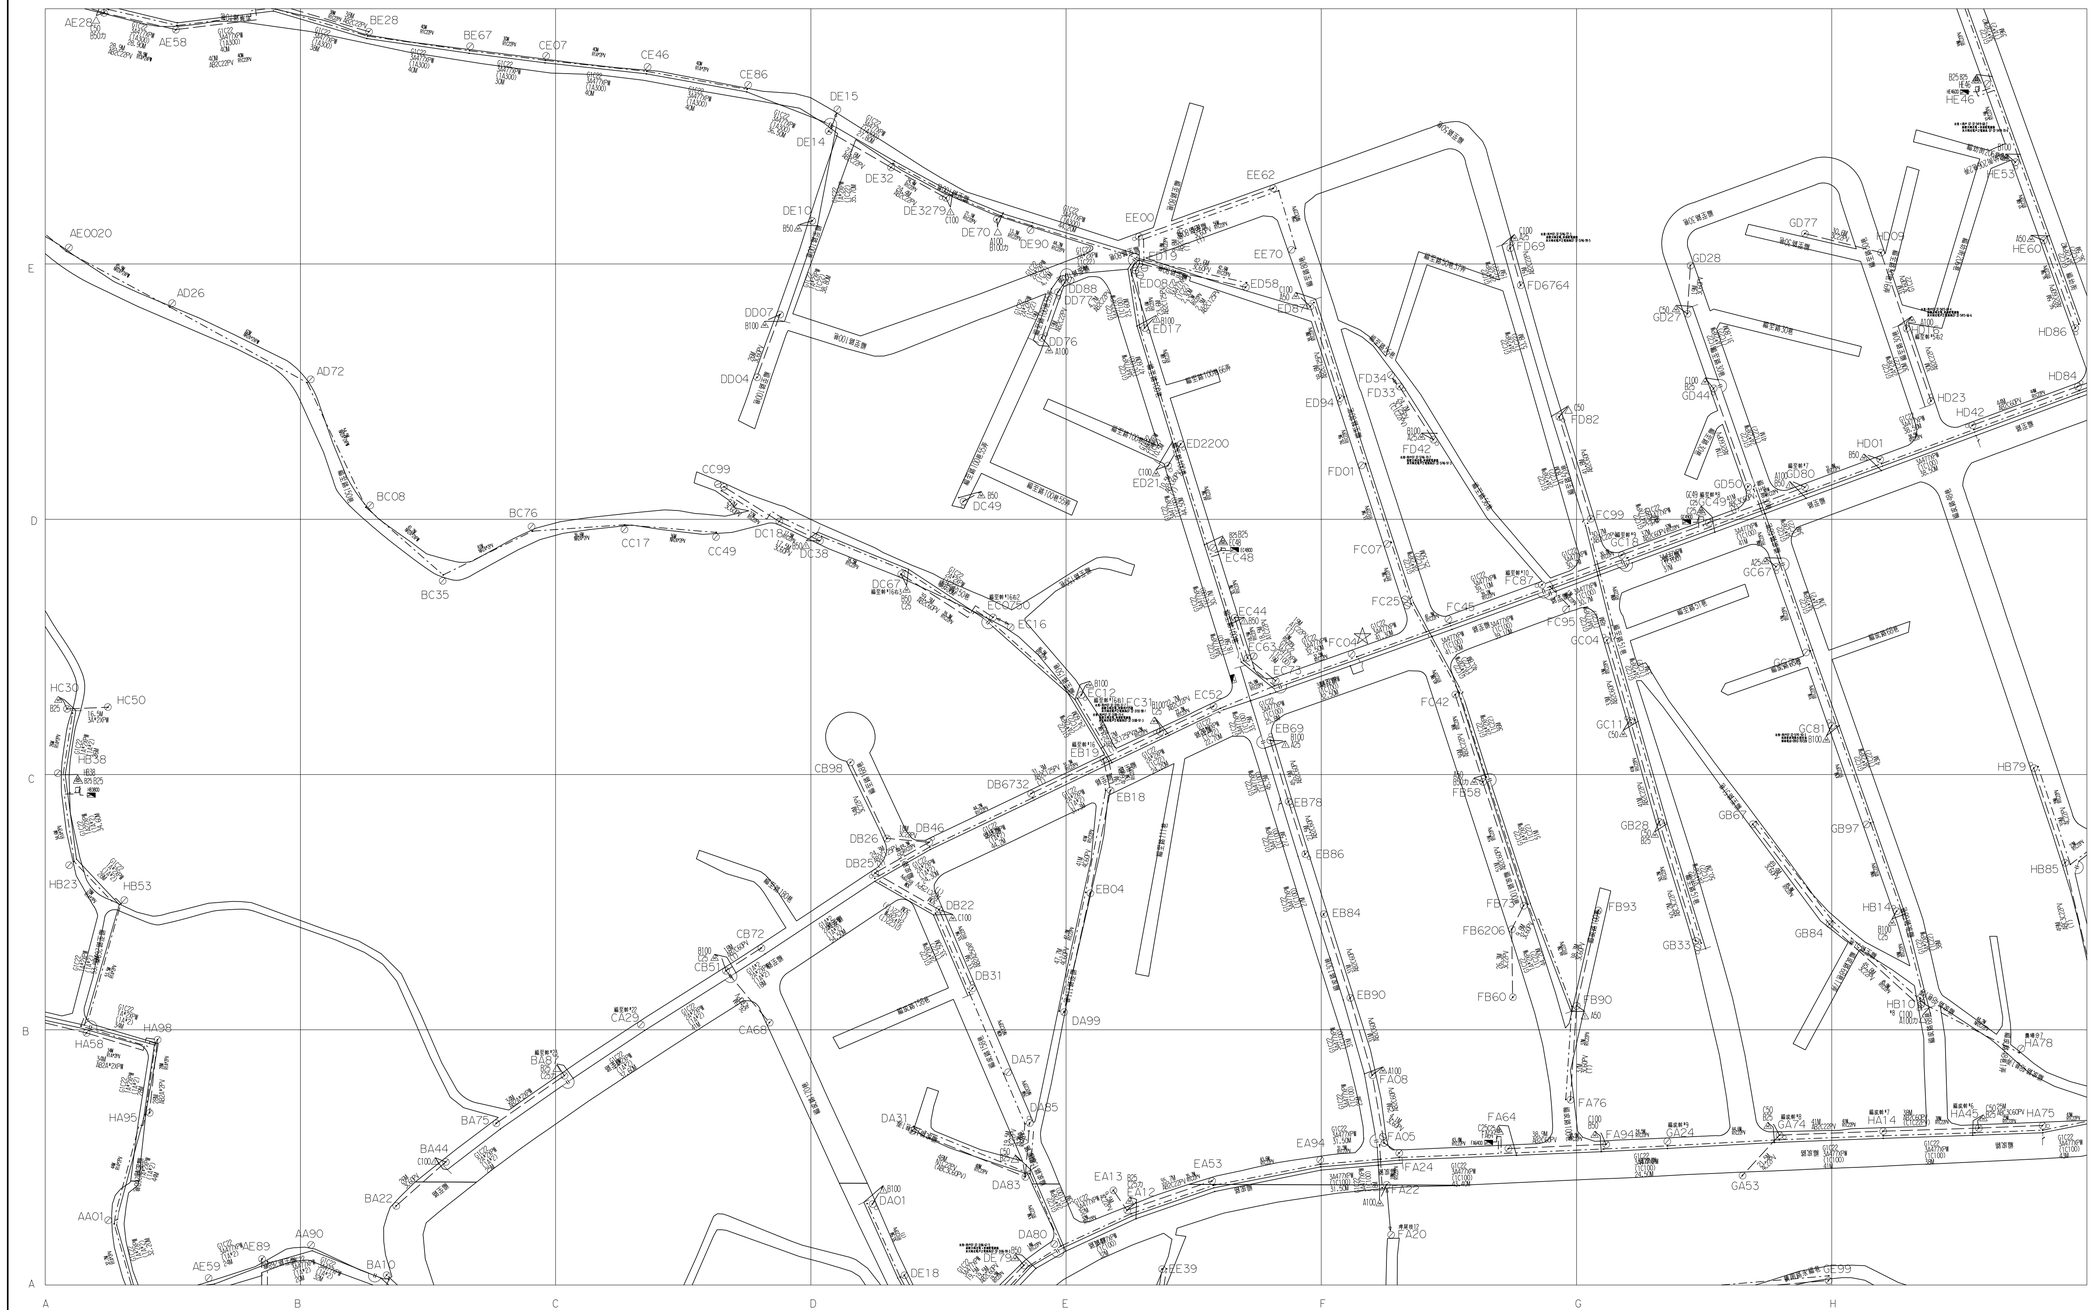


修正者	修正日期

供電變電所	
變電所別	供電饋線別

4261	4361	4461
4260	4360	4460
4259	4359	4459

比例 1:1200

0 50 100M

臺灣電力公司臺中區營業處

校對		批准	
製圖		製圖年月	
圖號	G4360 HT-LT/OH		