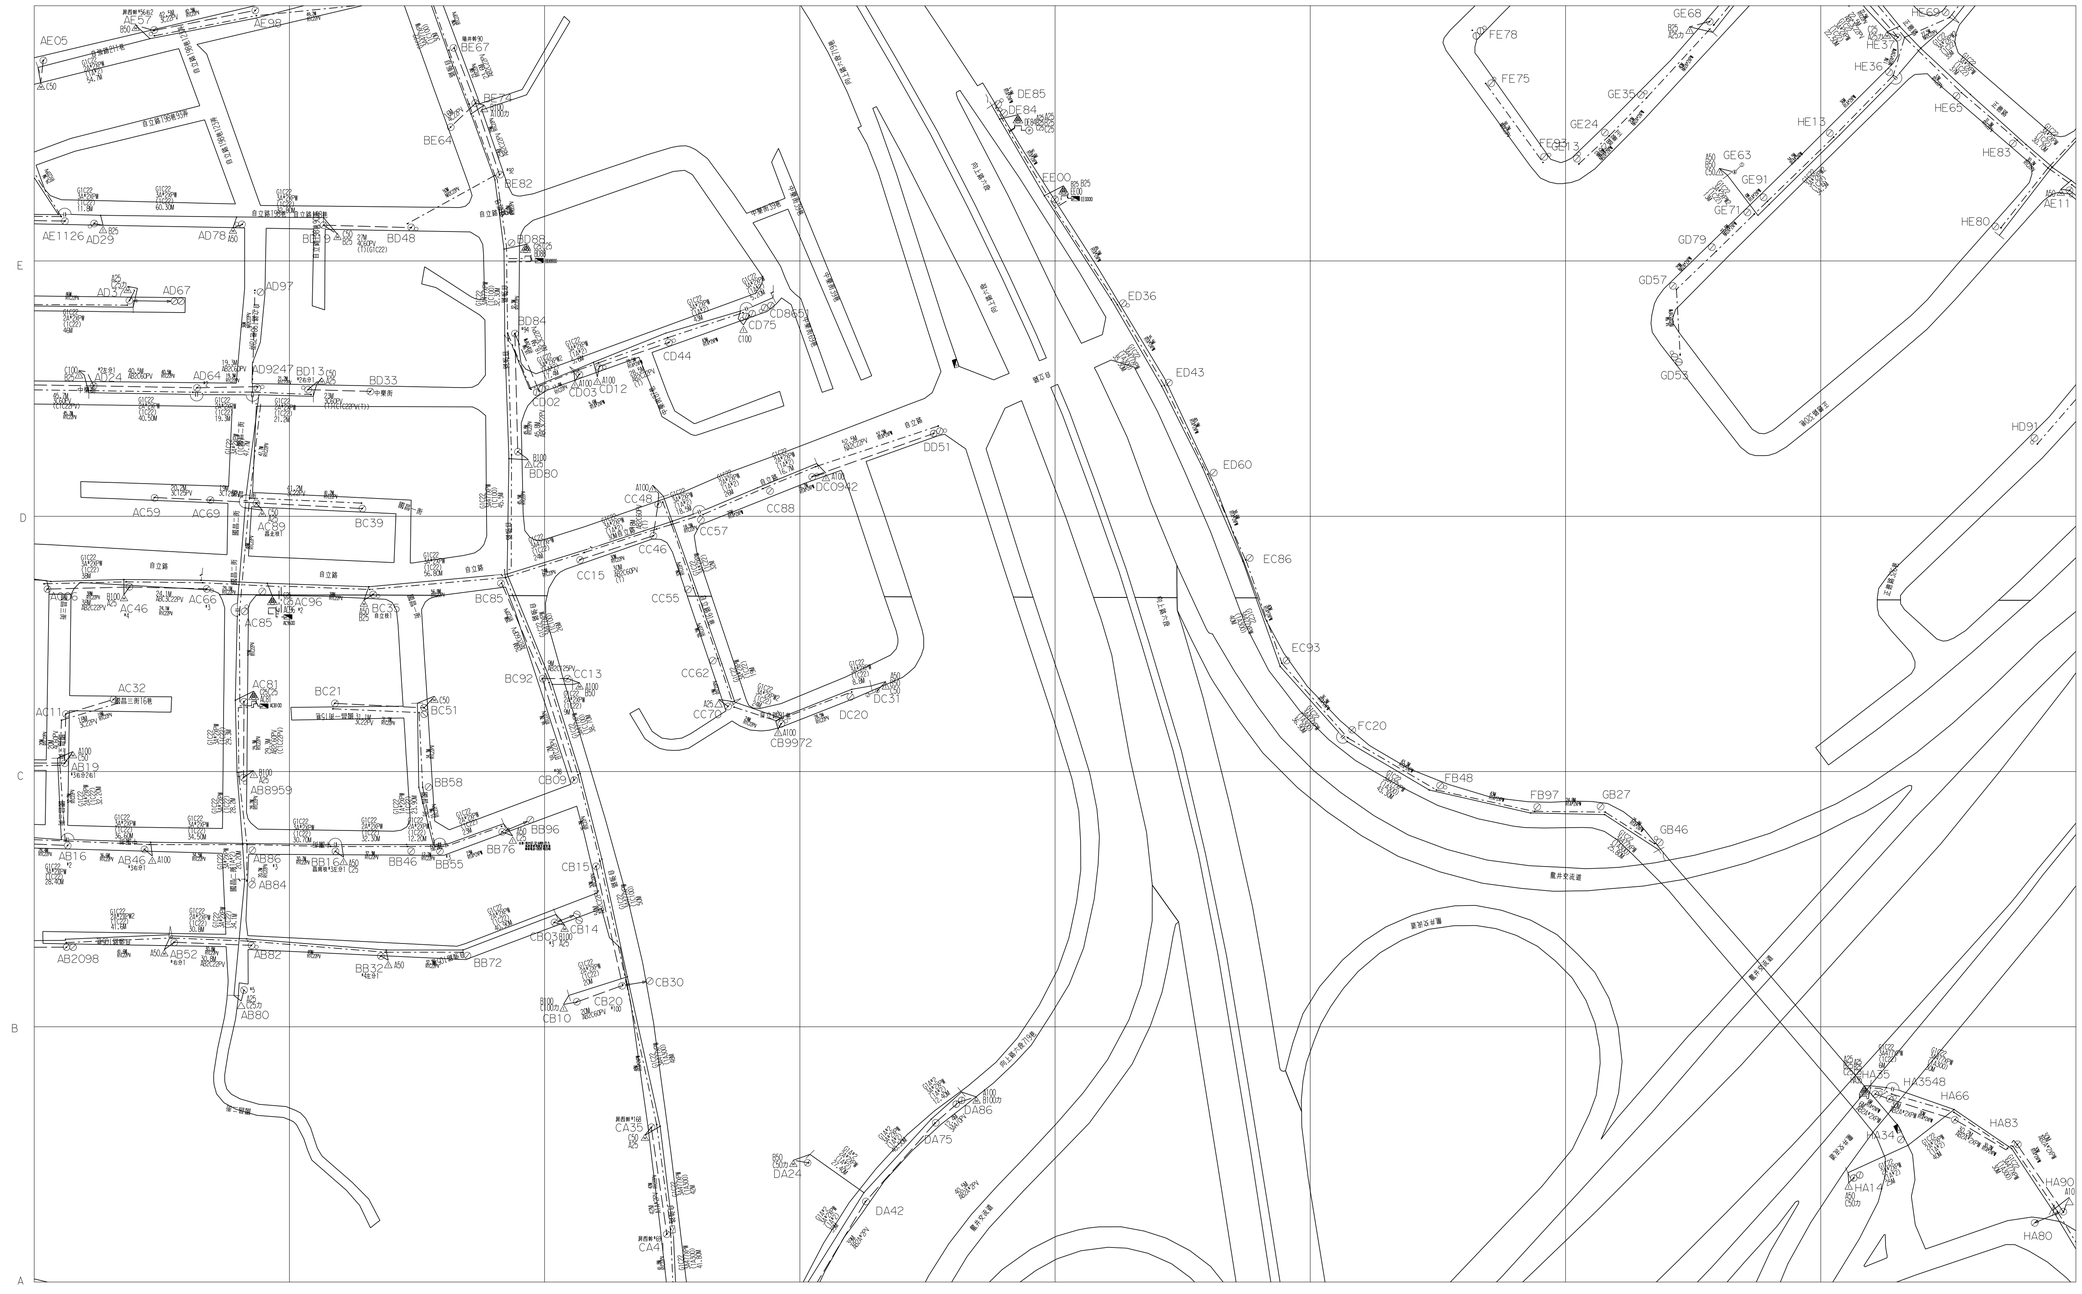


修正者	修正日期

供電變電所	
變電所別	供電饋線別

4355	4455	4555
4354	4454	4554
4353	4453	4553

比例 1:1200

0 50 100M

臺灣電力公司臺中區營業處

校對		批准	
製圖		製圖年月	
圖號	G4454 HT-LT/OH		