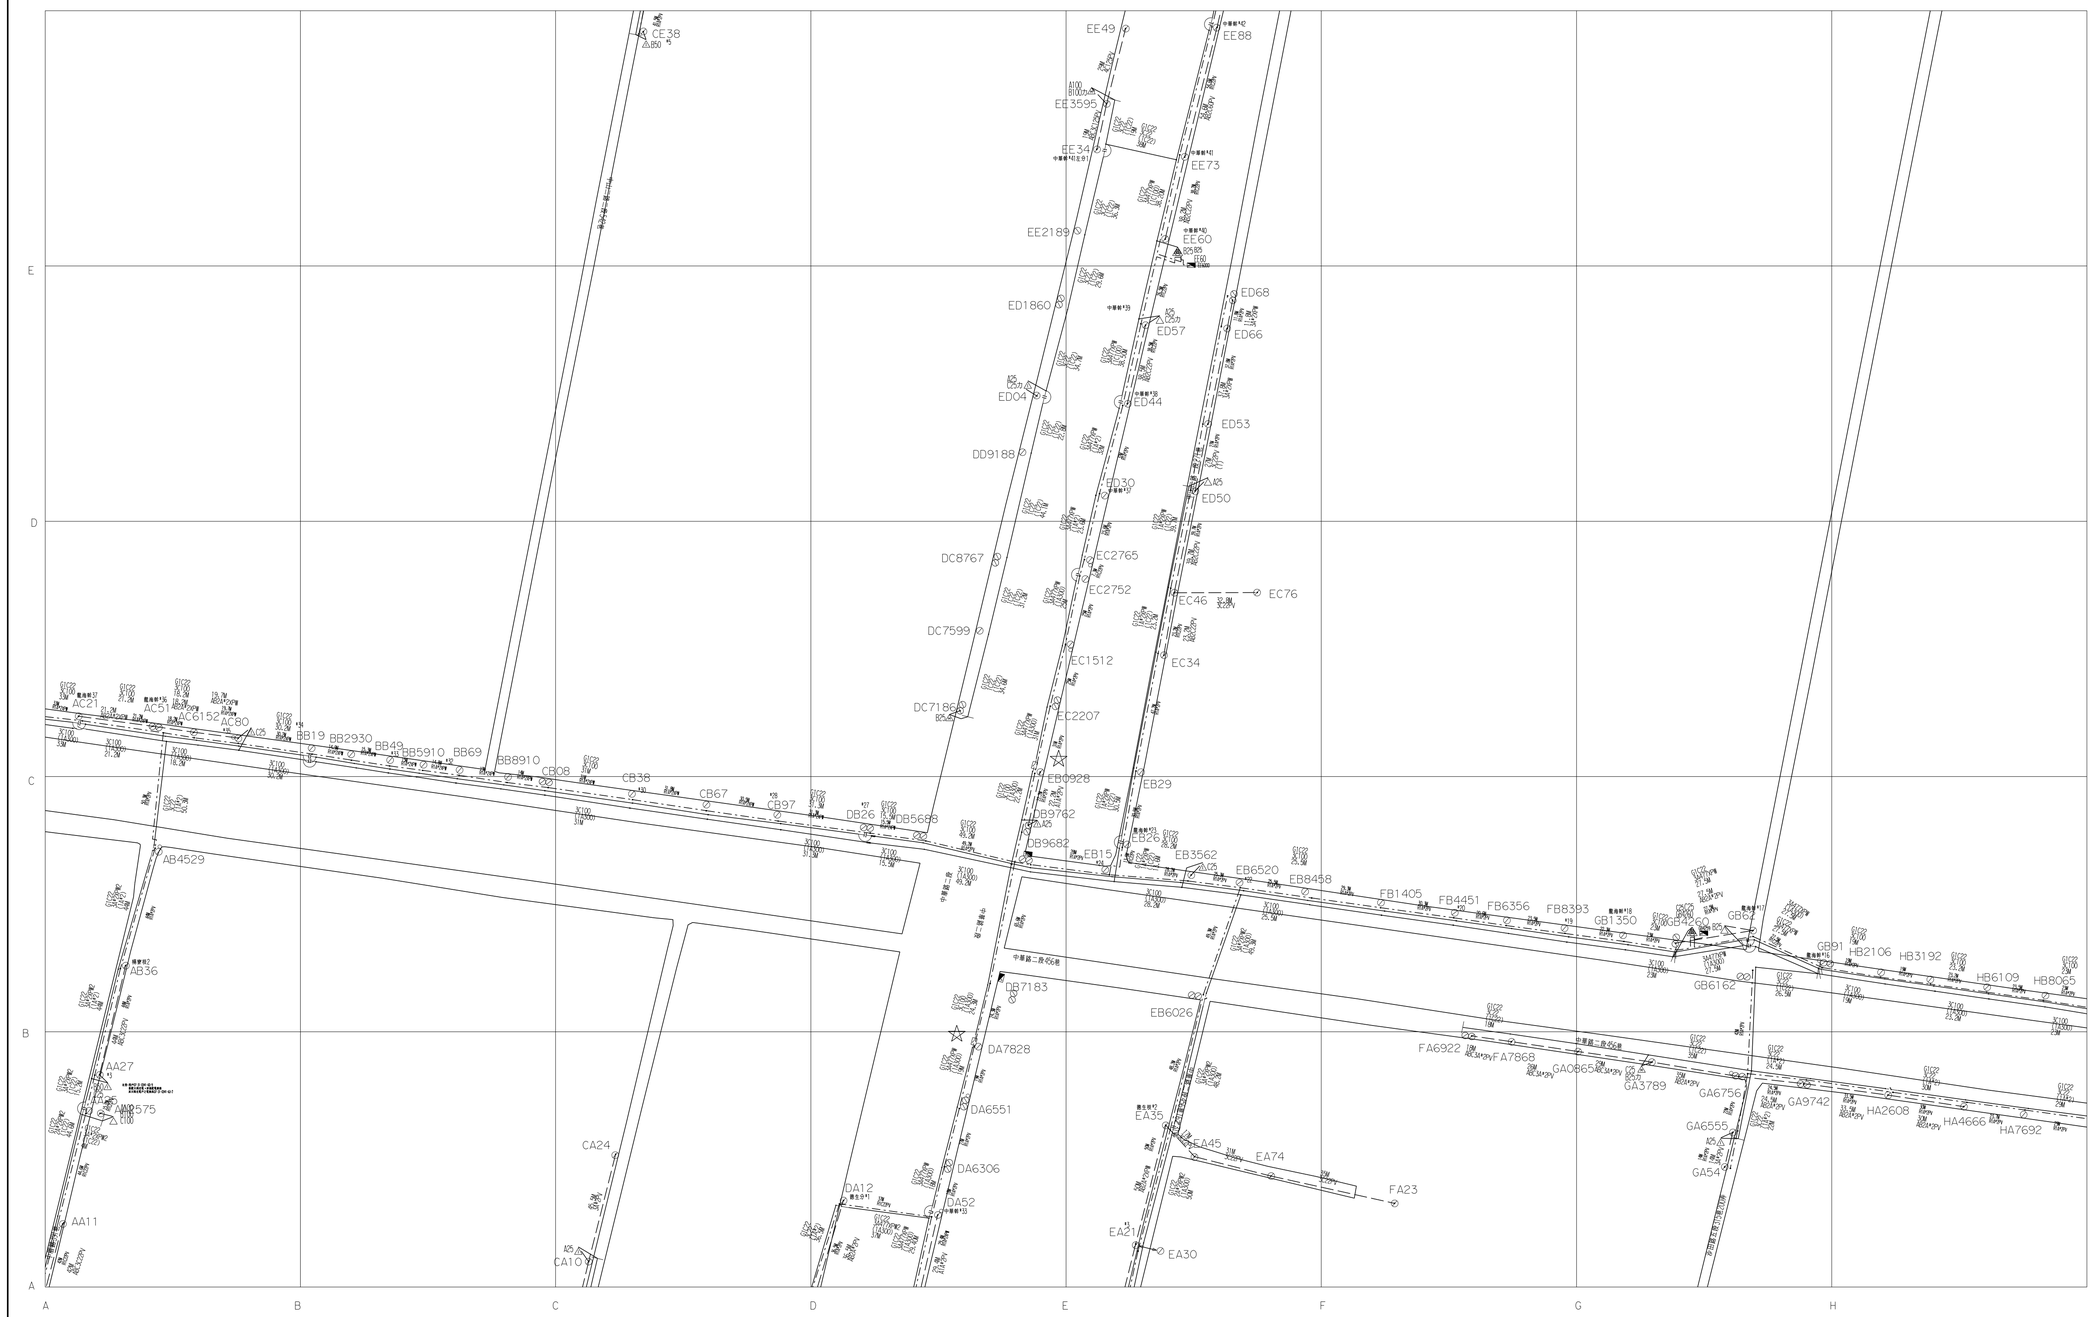



| 修正者 | 修正日期 |
|---|---|
| | |
| | |
| | |
| | |
| | |
| | |

| 供電變電所 | |
|---|---|
| 變電所別 | 供電饋線別 |
| | |
| | |
| | |
| | |
| | |
| | |
| | |

| | | |
|---|---|---|
| 3957 | 4057 | 4157 |
| 3956 | 4056 | 4156 |
| 3955 | 4055 | 4155 |

比例 1:1200

0 50 100M

臺灣電力公司臺中區營業處

| 校對 | | 批准 | |
|---|---|---|---|
| 製圖 | | 製圖年月 | |
| 圖號 | G4056 HT-LT/OH | | |