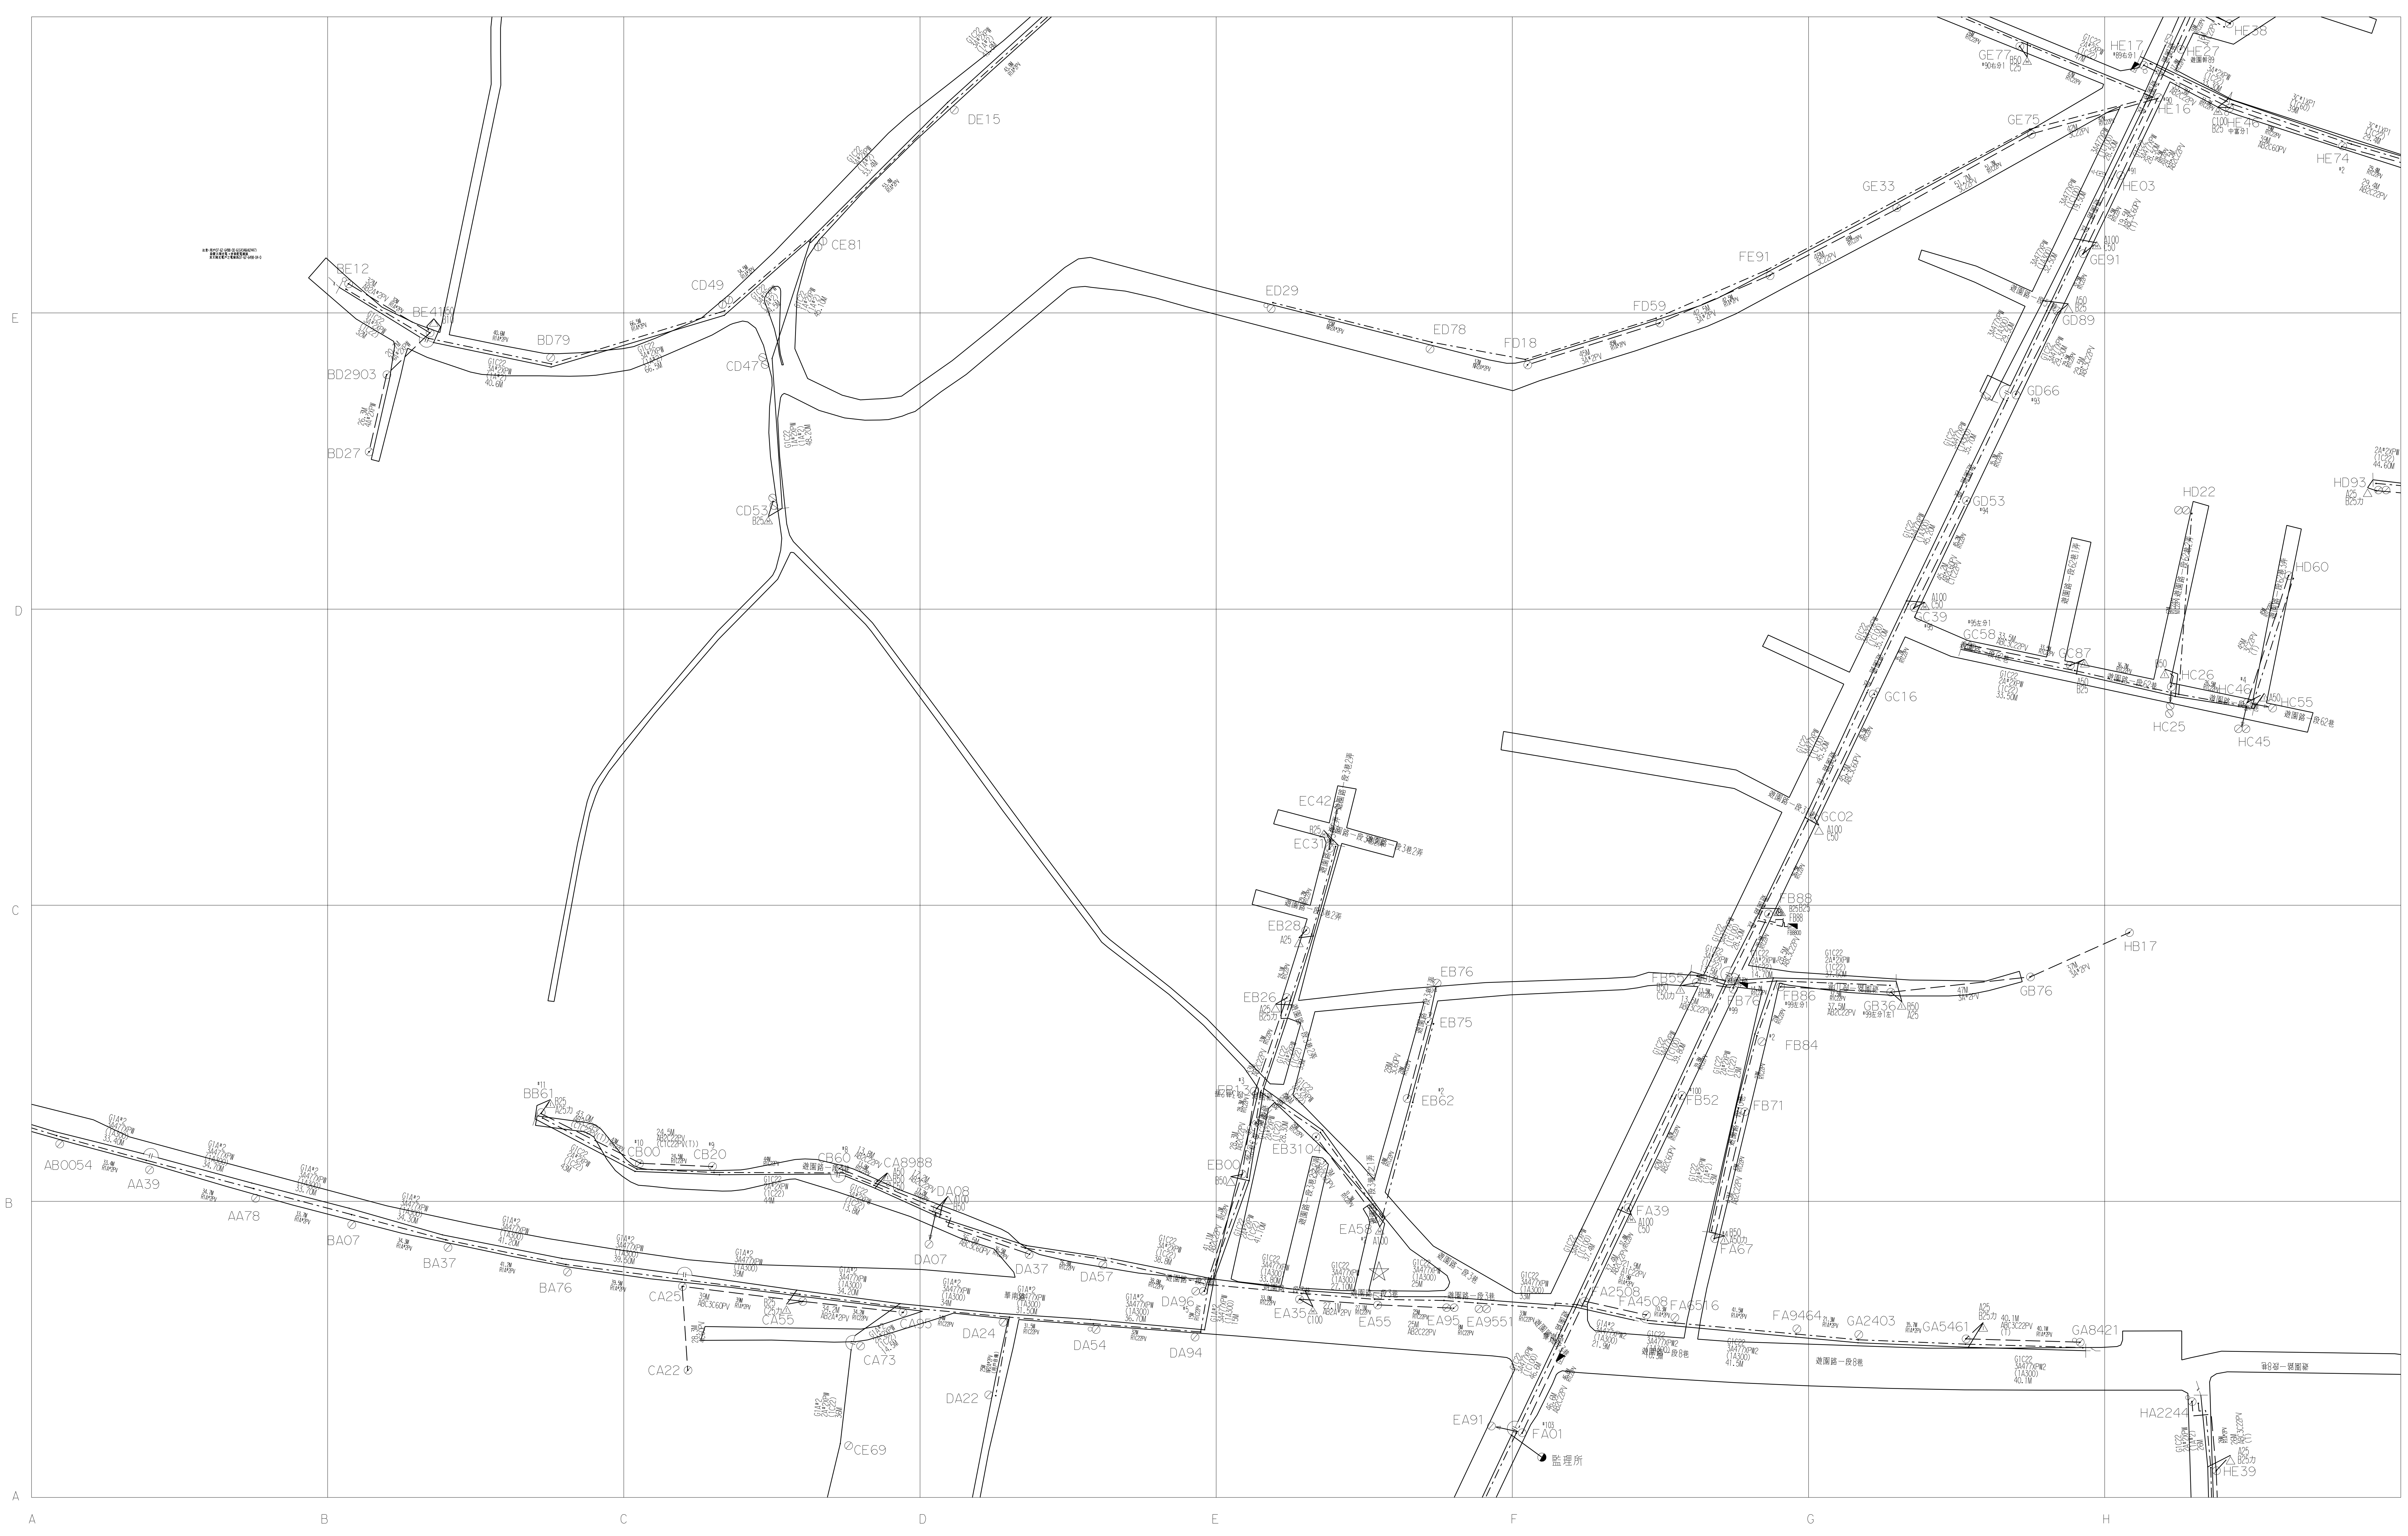

| 修正者 | 修正日期 |
|---|---|
| | |
| | |
| | |
| | |
| | |
| | |

| 供電變電所 | |
|---|---|
| 變電所別 | 供電饋線別 |
| | |
| | |
| | |
| | |
| | |
| | |
| | |

| | | |
|---|---|---|
| 4346 | 4446 | 4546 |
| 4345 | 4445 | 4545 |
| 4344 | 4444 | 4544 |

比例 1:1200

0 50 100M

臺灣電力公司臺中區營業處

| | | | |
|---|---|---|---|
| 校對 | | 批准 | |
| 製圖 | | 製圖年月 | |
| 圖號 | G4445 HT-LT/OH | | |