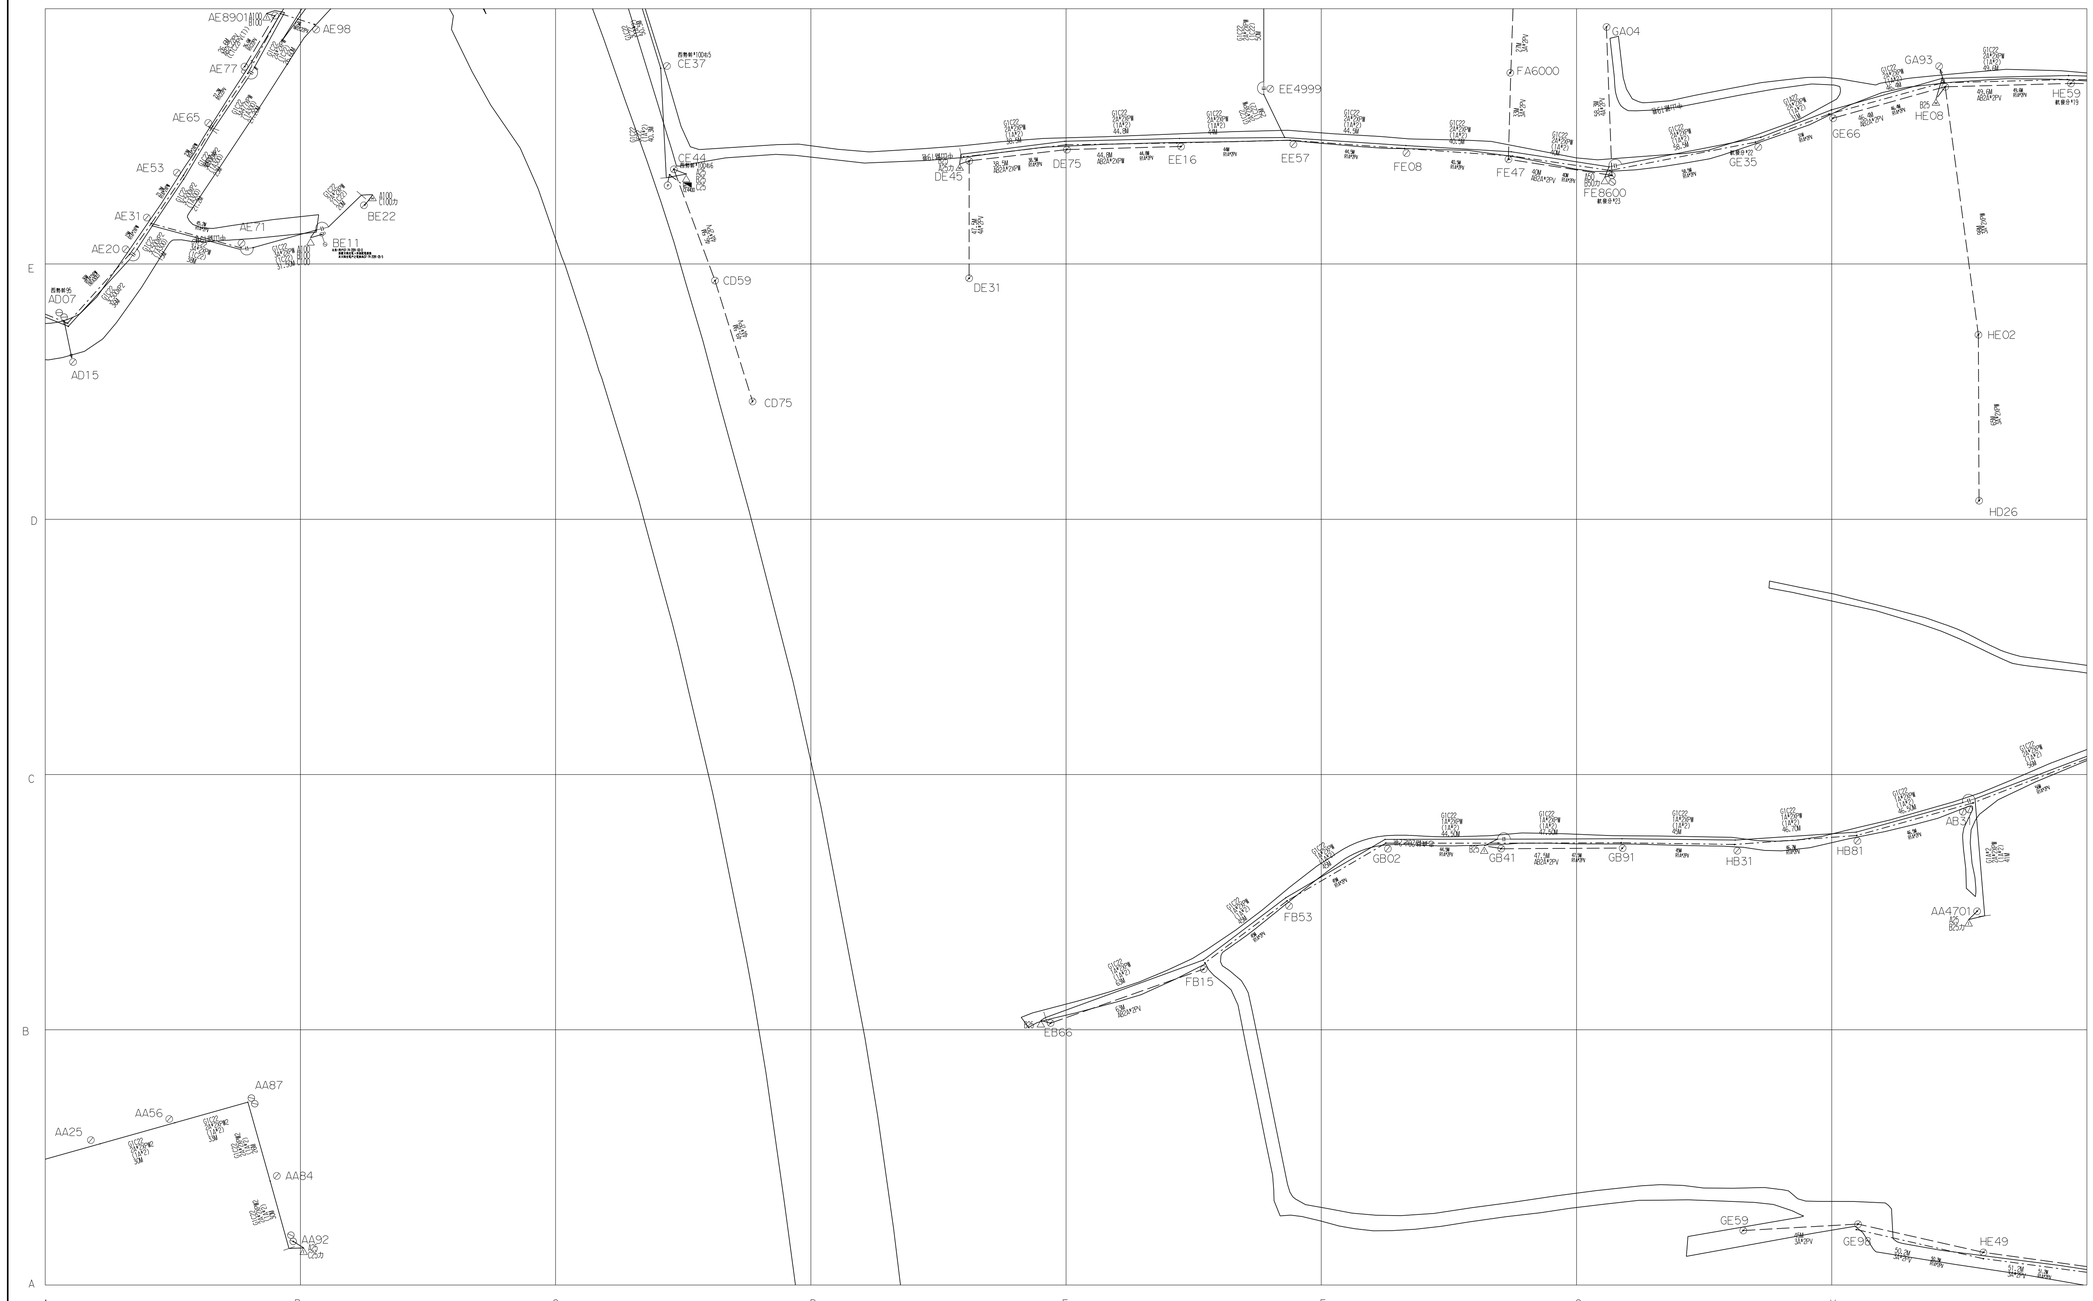


修正者	修正日期

供電變電所	
變電所別	供電饋線別

4665	4765	4865
4664	4764	4864
4663	4763	4863

比例 1:1200

0 50 100M

臺灣電力公司臺中區營業處

校對		批准	
製圖		製圖年月	
圖號	G4764 HT-LT/OH		